城市绿脉——高层办公及商业综合体设计


Urban green veins —— High-rise office and commercial complex design

姓名：刘欣越
班级：建筑学1班
学号：6018204106

设计说明： 该商务中心设计致力于打造一条商业，纽带串联起滨海新区的古今文脉，为于家堡金融中心注入新鲜血液，与普通商务楼不同的是，该设计提取海的元素，并与垂直森林概念结构结合，为高楼林立的响螺湾注入一丝新鲜的活力，并为各年龄层游客提供娱乐休憩场所。




项目背景

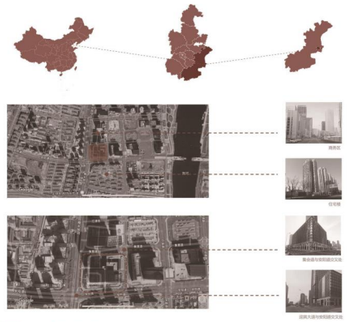


项目位于中国天津市滨海新区新区响螺湾商务区。海河南岸的响螺湾地区，位于大沽地区的新城镇卫星城，是滨海新区中心商务商业区的起步区，北依海河岸线，与海河外滩公园隔河相望，东沿海河与滨海新区中心商务商业区于家堡商务区毗邻，西至中环干道河南路，南抵主干公路津沽一线。地块位置正处于滨海新区响螺湾中心商务商业区C-11地块。四至范围为：东为规划路、南至安阳道、西为迎宾大道、北为安阳北道。

区位分析

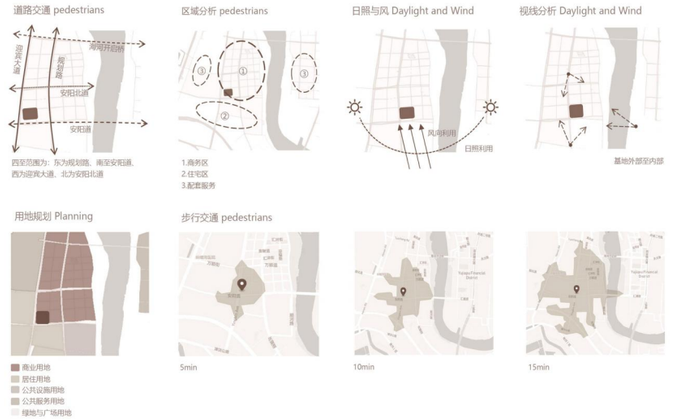


周边分析

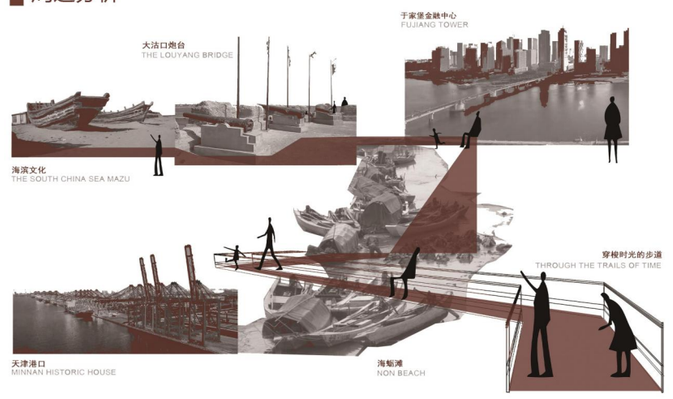

项目地点位于滨海文化集中地，周边配套设施多样，是重点建设各省市及中央企业驻滨海新区办事机构及配套服务设施，除拥有一系列现代化星级宾馆和商业广场的现代化建筑外，还是天津港所在地以及大沽口炮台遗址所在地，人文历史气息浓厚，周边配合中央水体公园，将成为天津滨海新区未来新的地标建筑群落。

人群需求

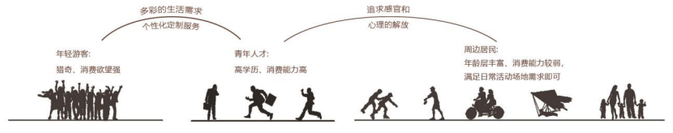

经济技术指标

容积率：2.79

建筑密度：31.7%

建筑高度：96.6m


总建筑面积：69814㎡

地上建筑面积：51079.5㎡

地下建筑面积：18734.5㎡




设计概念

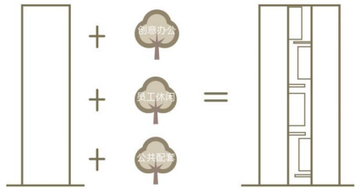

考虑项目所在场地界面，基于景观视野与城市延申面的考量，设计时在写字楼的开放区域植入绿化，休闲平台，屋顶花园以及方盒子、艺术楼梯等创意特色空间，在延续的垂直绿化中形成公共互动空间，与内部的办公空相互形成呼应。同时，拥有开阔视野的高层办公楼可眺望滨海美景。

总体架构

1.路口交汇处人流量较大

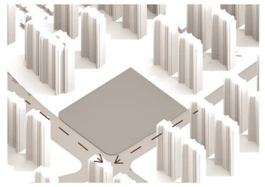

2.规划写字楼与裙房大致体量



3.划分场地区域



4.根据地形设计建筑物大致形状




5.垂直绿化与室外台阶引入




6.方案生成




总平面图1：500

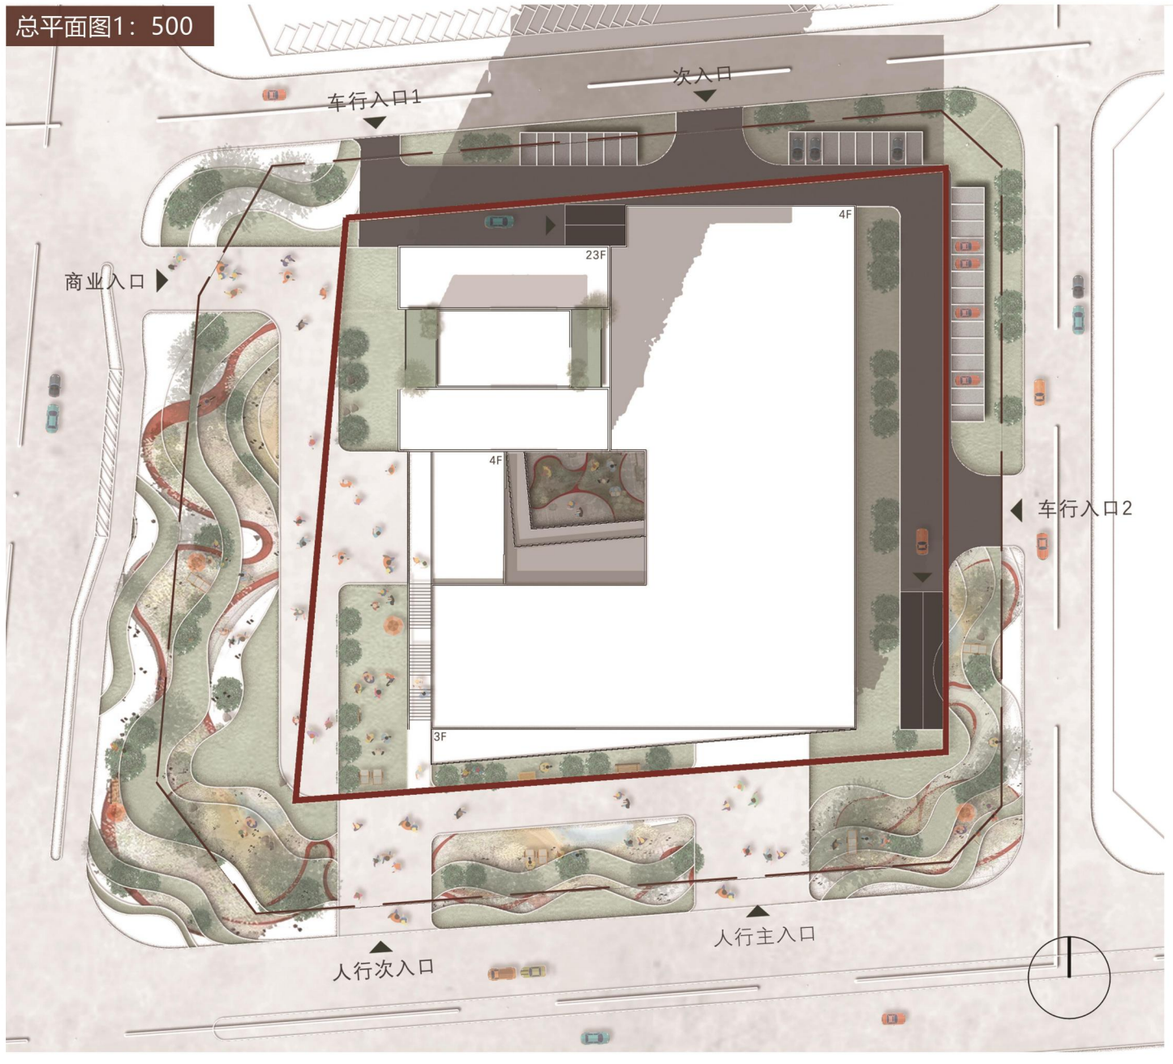



低区平面图1：300

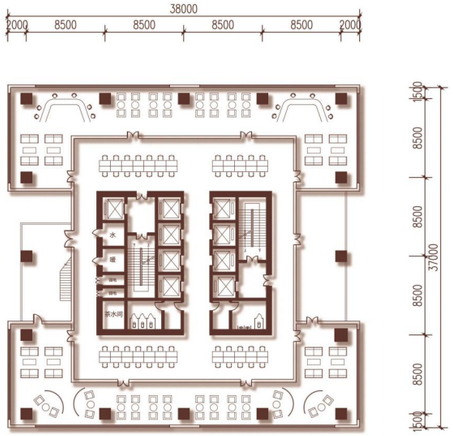

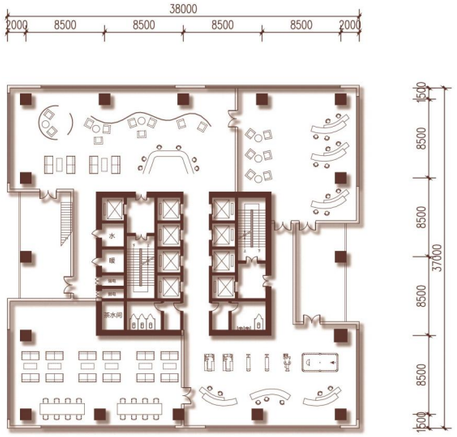


高区平面图1：300

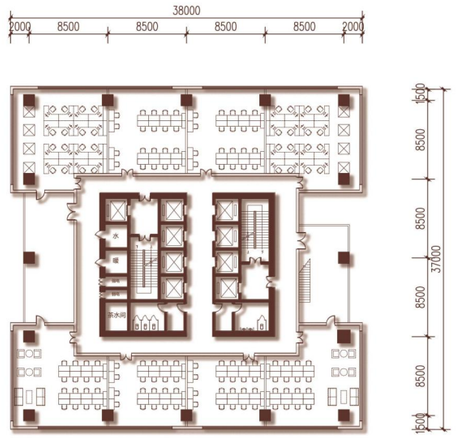

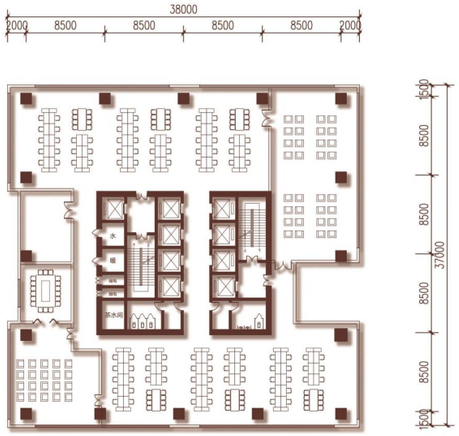

南立面图1：300

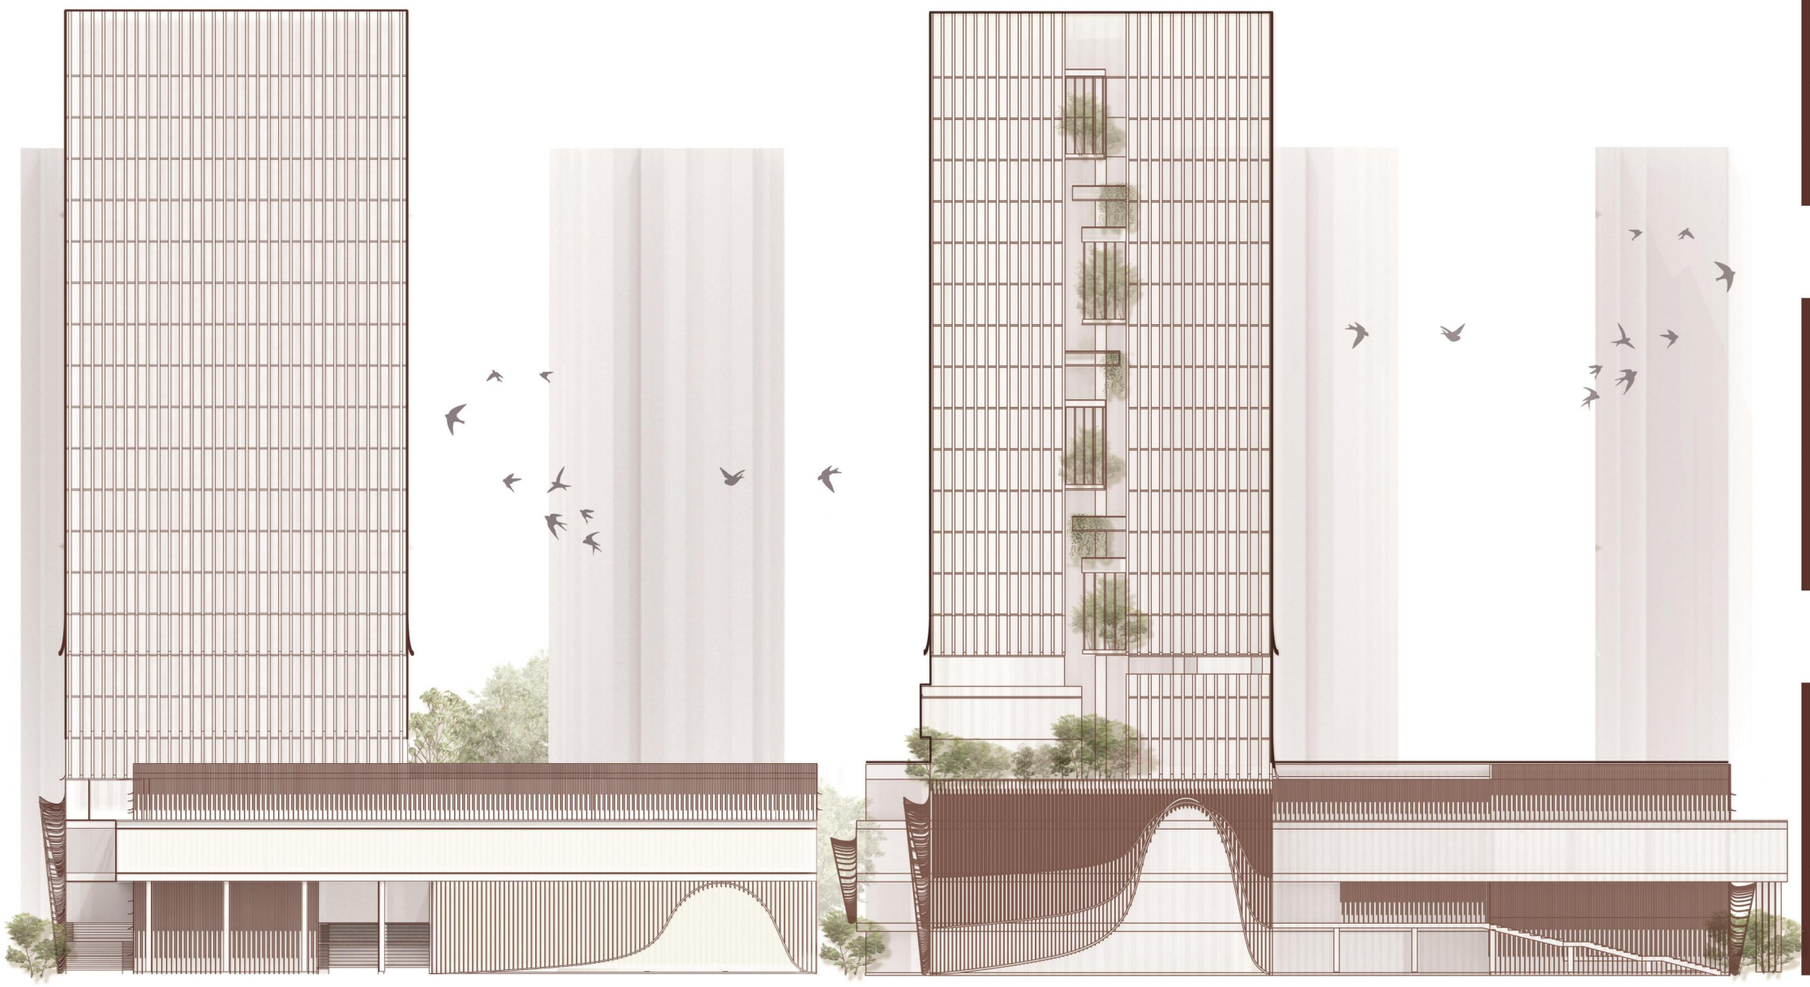


西立面图1：300

入口广场效果图



垂直绿化效果图

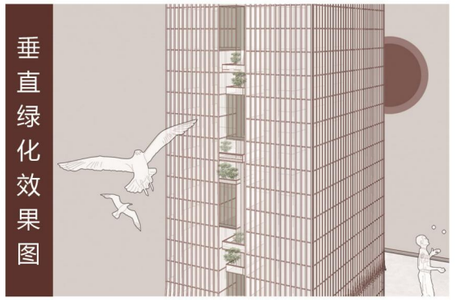

室外平台效果图



建築學1班 劉欣越 6018204106

長樂雅頌

ELEGANCE OF SONG

—探寻全年龄化居住新模式

EXPLORE A NEW MODEL OF FULL-AGE HOUSING



區位分析



中國·天津



南開區



南開大學
迎水道校區舊址

住戶行為分析

飲食





會客

休憩





玩耍

解決策略

雙減政策下的陪伴空間 — LDKG一体化 — 房间相互渗透，实现空间的串联

中國家庭的全生命周期 — 模块化套间 — 满足各年龄段家庭成员居家模式

適老設計的改造和研究 — 老人房朝南
独立卫浴间
双床设计 — 充分的光照有利于老人的健康
老人起夜不会影响其他家庭成员
互不打扰，满足互相尊的生活

現狀問題

- 后疫情时代人们生活模式被重塑
- 三胎时代居住单元功能性需加强
- 居住观念和消费能力的不同级配
- 新生代家庭对多元化生活的诉求

中國式家庭關系



孝親

想要照顾儿孙，也想要互不打扰的生活

安享晚年的的60后



理解

想要照顾好家人，也想保留自身爱好，关爱自身身心

上有老下有小的80后



教育

想要自己的独立空间，也想和兄弟姐妹一起玩要

共同成长的兄弟姐妹



接納

想要磨合融入三代人的家庭

宇宙最强辅助育儿嫂

幫忙照顧

老人作为家庭重要成员，候鸟式往返照看儿童的同时也是一个家庭的重点关心对象

相互扶持

男女主人作为奋斗主力军，兼顾老中青三代，既要共享空间也要独立格调


彼此陪伴

孩子作为家庭中心，且不同年龄段教育方式有所不同，也需要不同尺度的活动空间

輔佐照料

育儿嫂作为家庭最强辅助，协助主人照顾孩子，也扮演着照顾家庭饮食起居的重要角色

立面生成

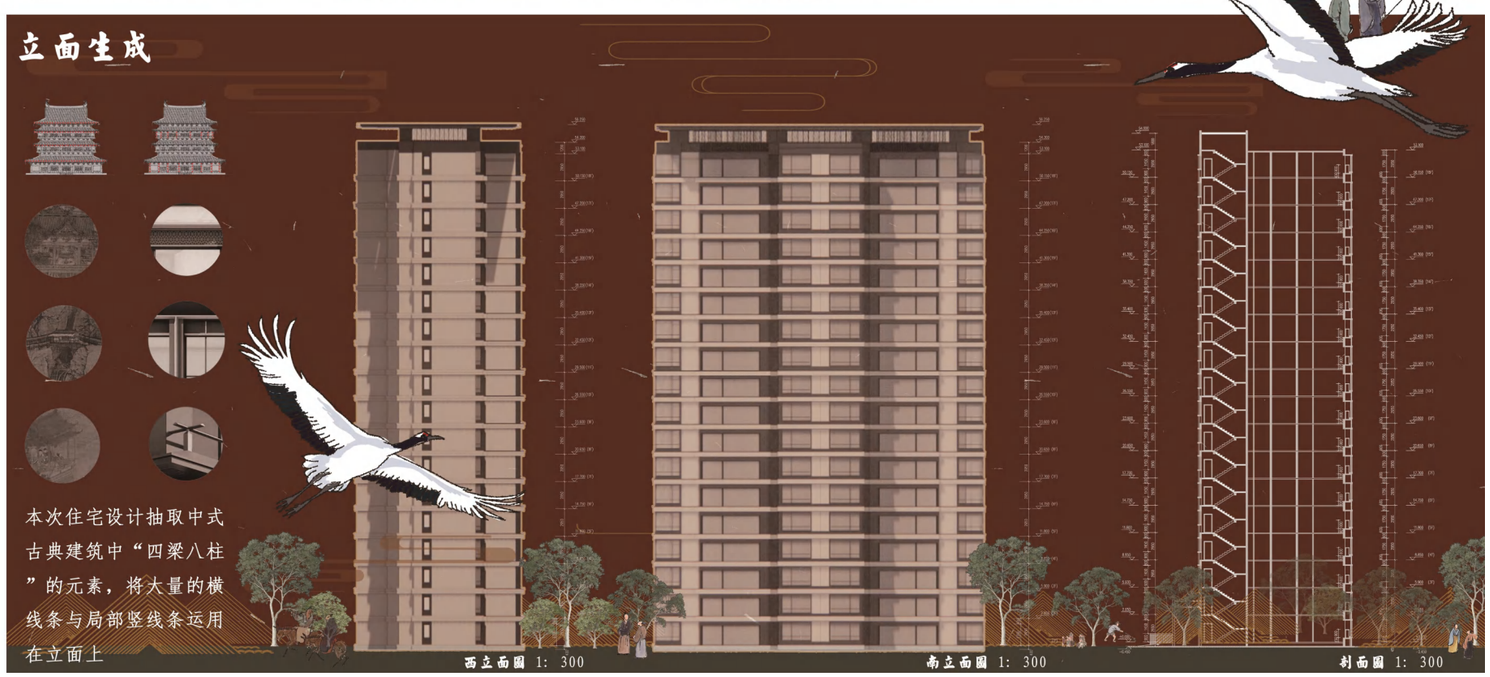


本次住宅设计抽取中式古典建筑中“四梁八柱”的元素，将大量的横线条与局部竖线条运用在立面上


西立面圖 1: 300　南立面圖 1: 300　剖面圖 1: 300

建築學1班 劉欣越 6018204106


首層平面圖

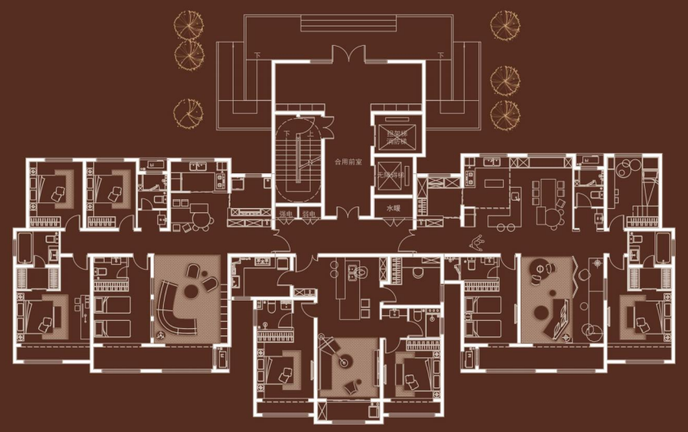


標準層平面圖

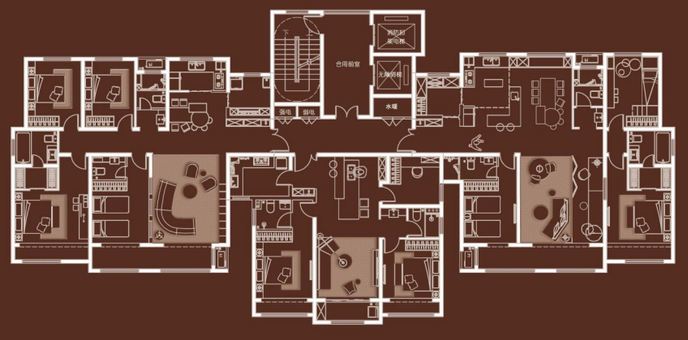

屋頂層平面圖

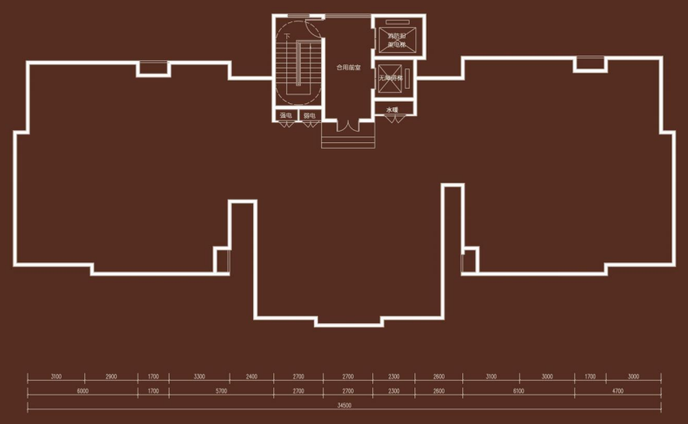


戶型A

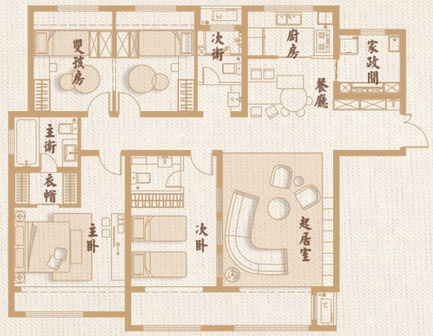


套內使用面積	公攤面積
143㎡	22.1㎡

戶型B

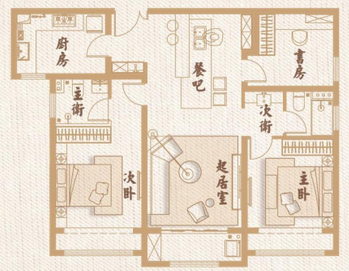

套內使用面積	公攤面積
94㎡	14.5㎡

戶型C

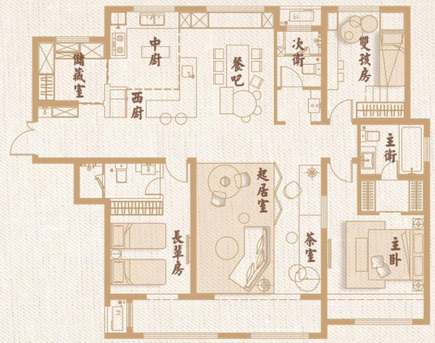

套內使用面積	公攤面積
143㎡	22.1㎡

主人色彩

“小歡喜”式家庭

- 兩代四口或五口之家，有三胎計划
- 老人经常探望孩子，有育儿嫂协助

關注親子活動　　強調生活共享

“都挺好”式家庭

- 兩代三口之家，追求极简生活
- 老人分开居住偶尔来帮忙

關注家庭生活　　強調品質生活

“過把癮”式家庭


- 兩代四口或五口之家，有三胎计划
- 老人长居在家，帮助儿女照顾孙辈


關注生活情趣　　強調品質格調







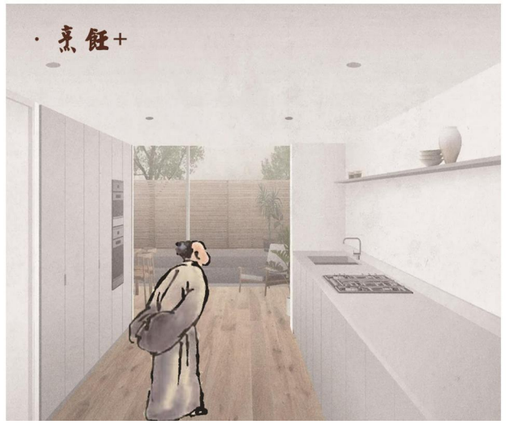

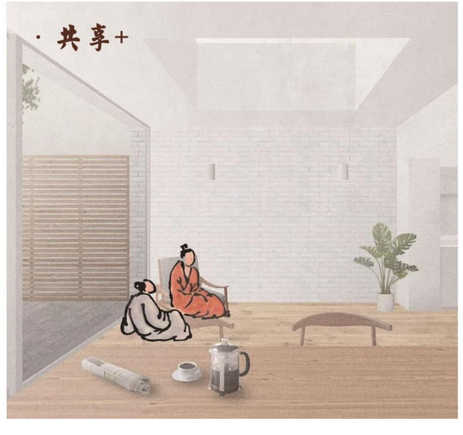





整体鸟瞰图




概念演绎

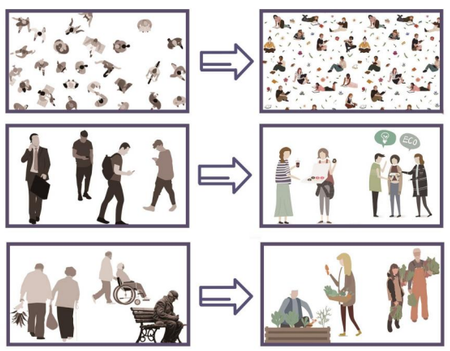


周边价值分析

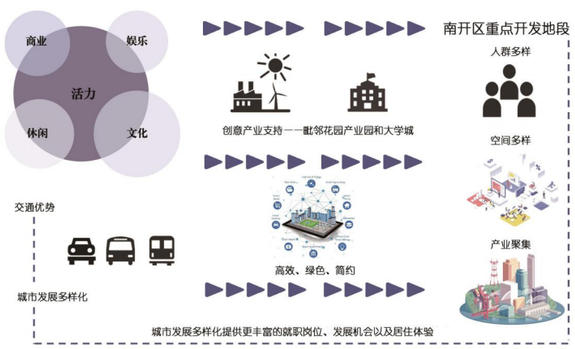



区位分析

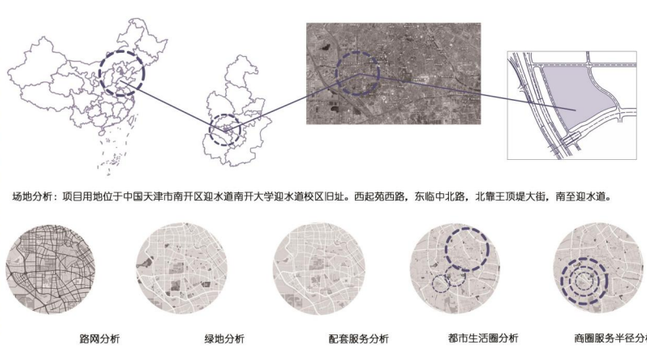


场地周边环境分析

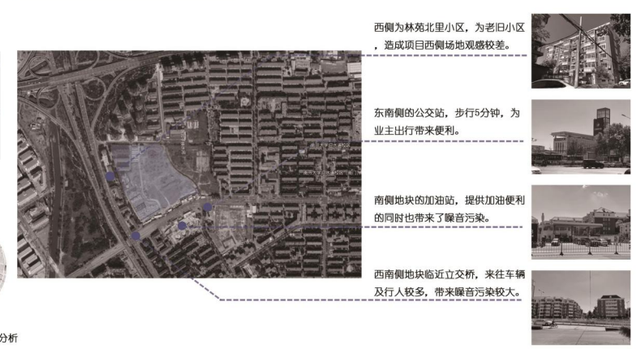


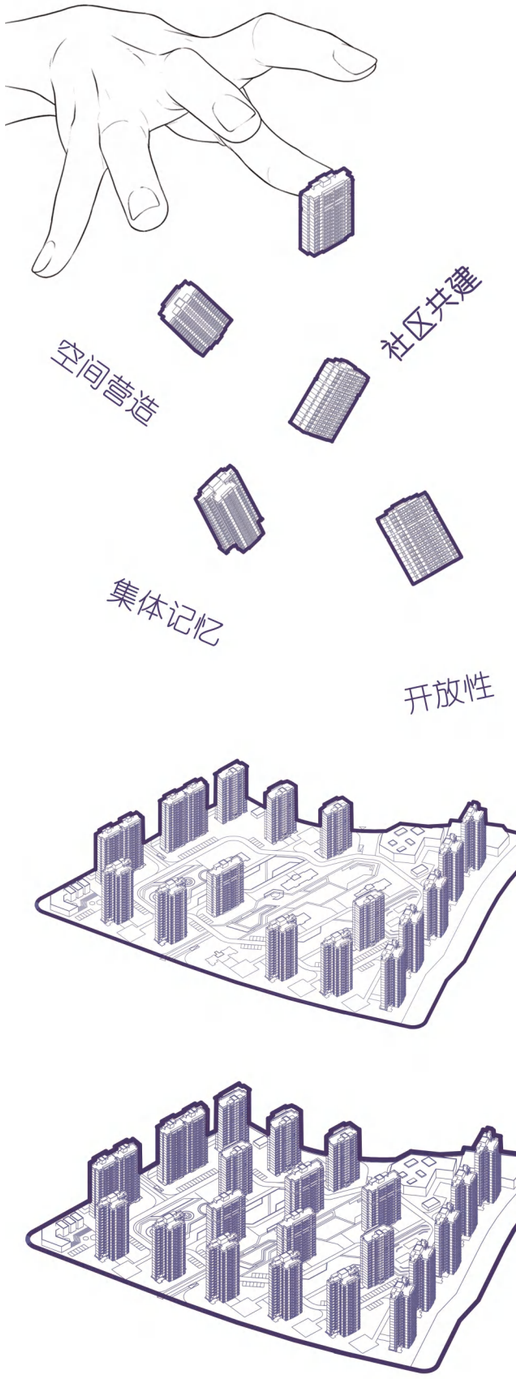

空间营造
社区共建
集体记忆
开放性

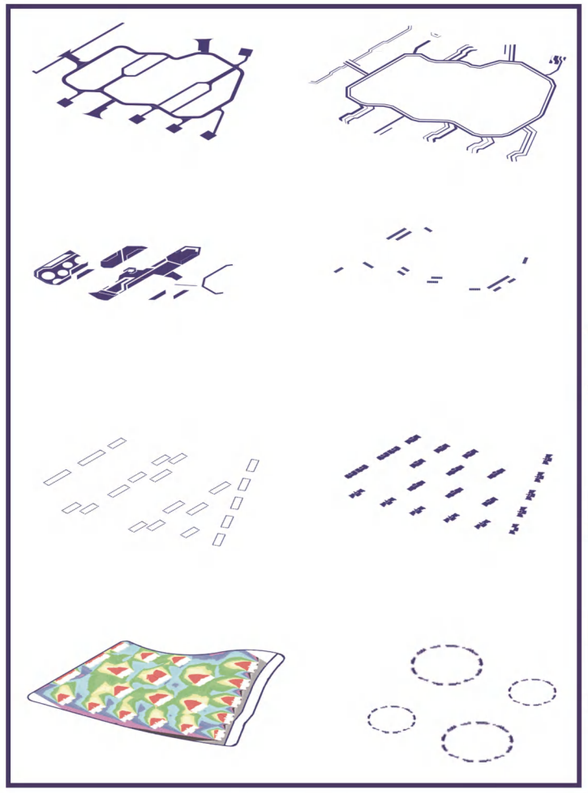



人群混居意向
两室/小三户的人才公寓
三户室的温馨住宅
四室户的品质雅居

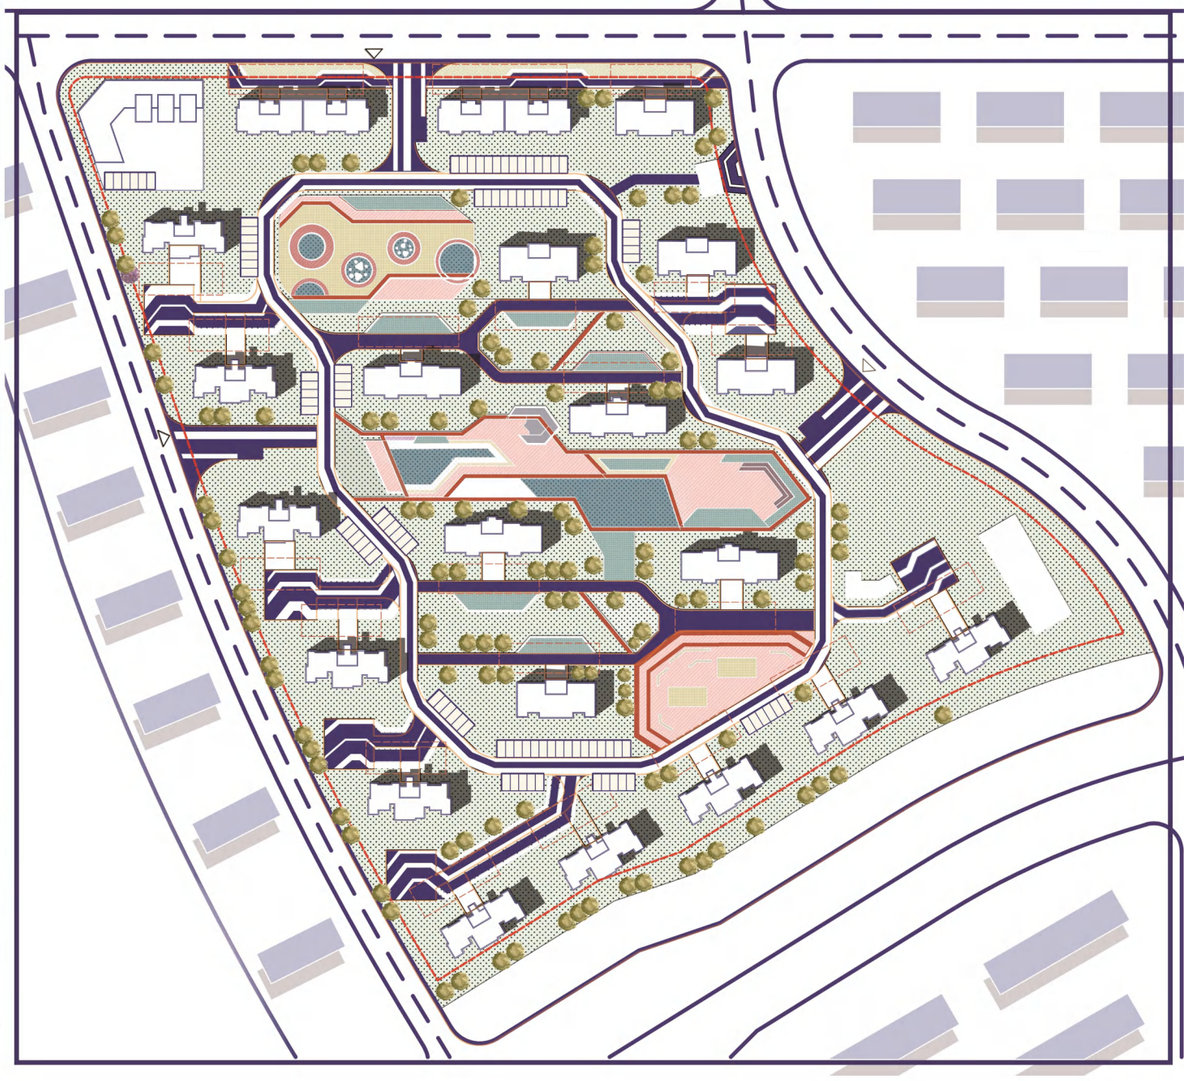

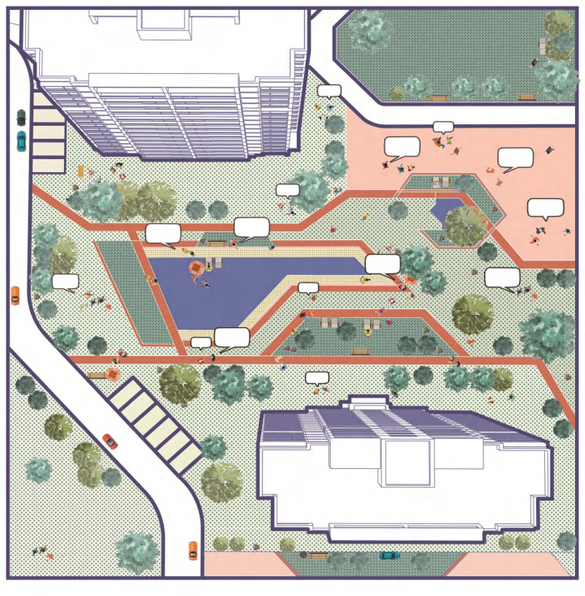

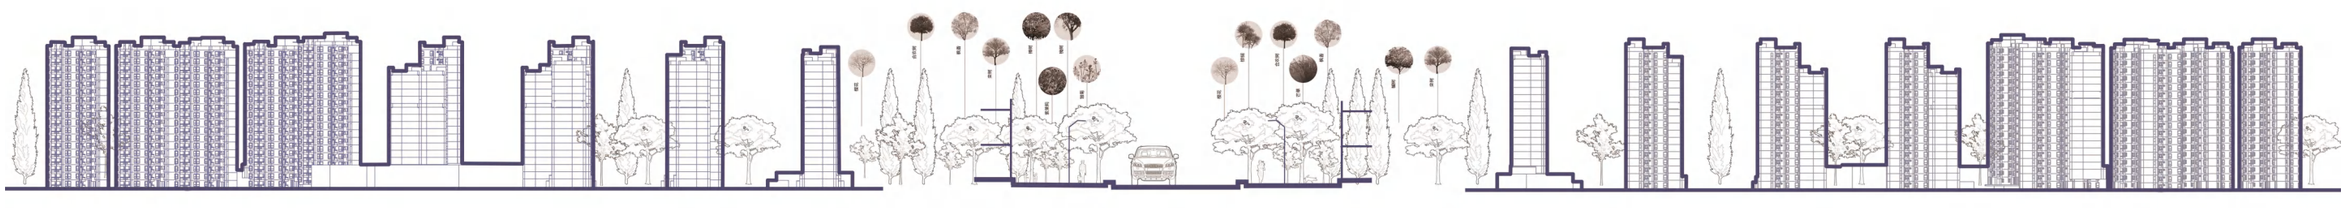

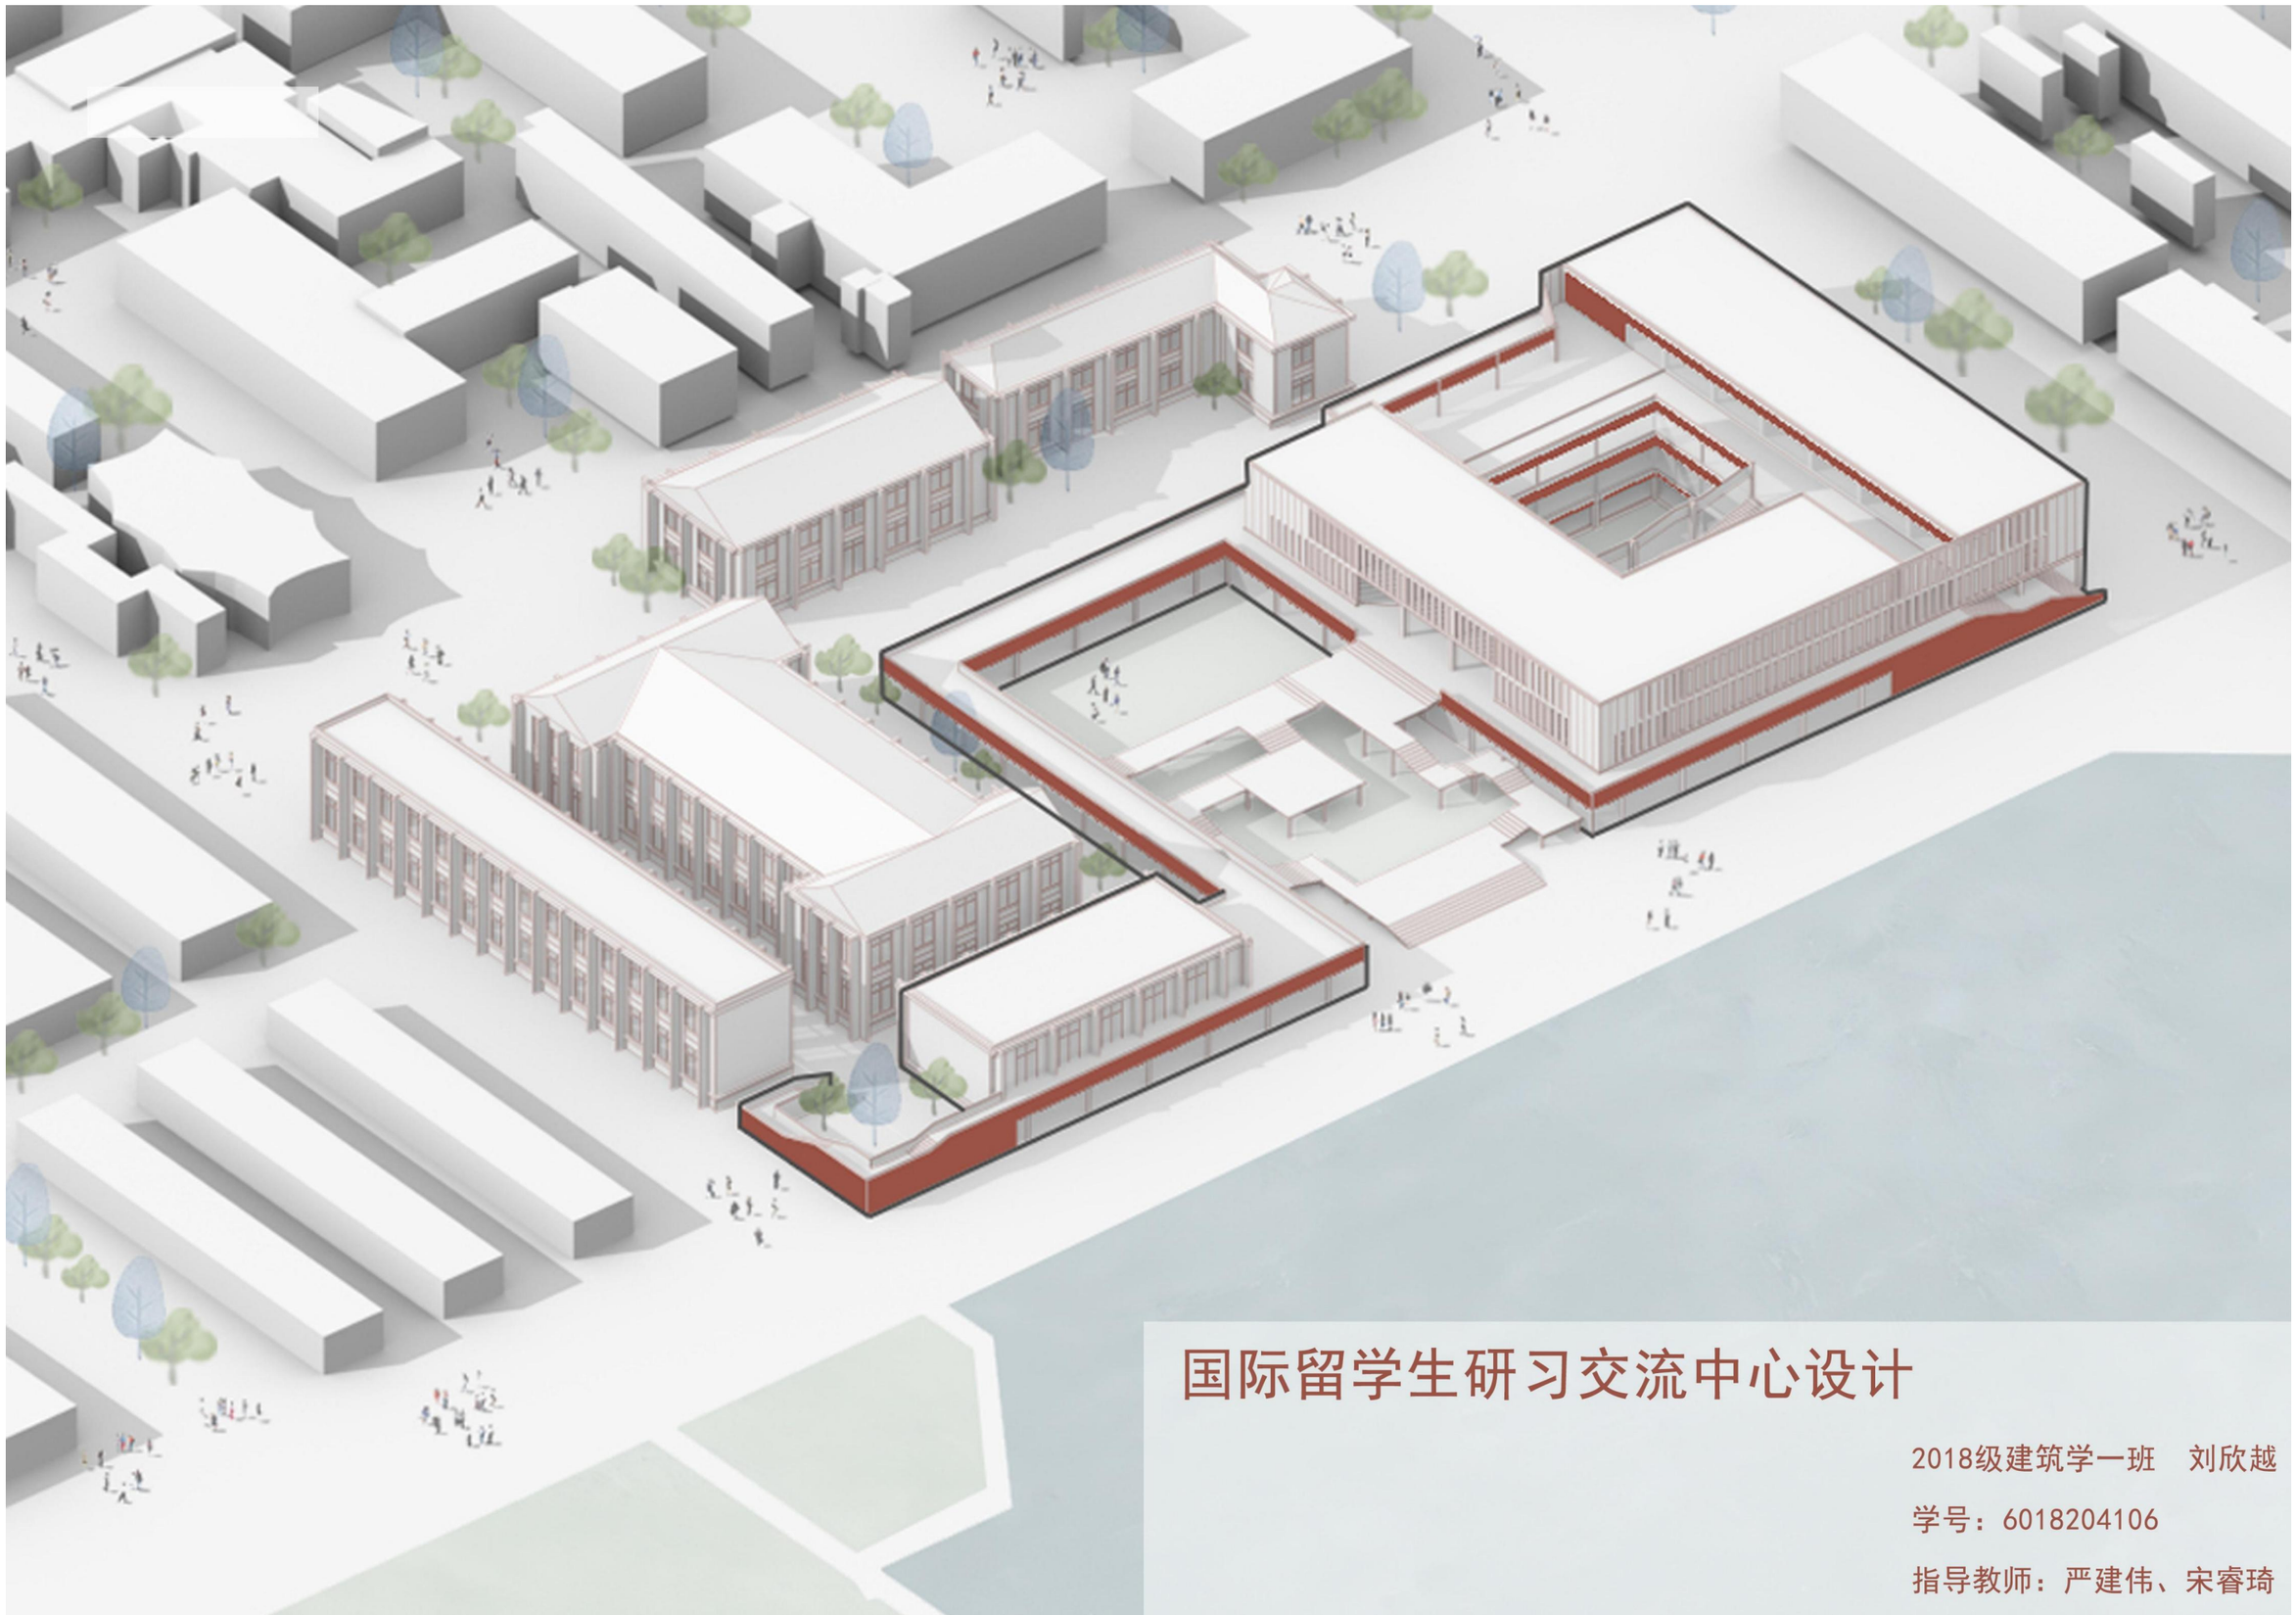

国际留学生研习交流中心设计

2018级建筑学一班　刘欣越

学号：6018204106

指导教师：严建伟、宋睿琦

· 场地文脉分析

1895

天津大学，前身为北洋大学


始建于1895年，是中国第一所现代大学。



1951

1951，北洋大学与河北工学院合并后

更名为天津大学。

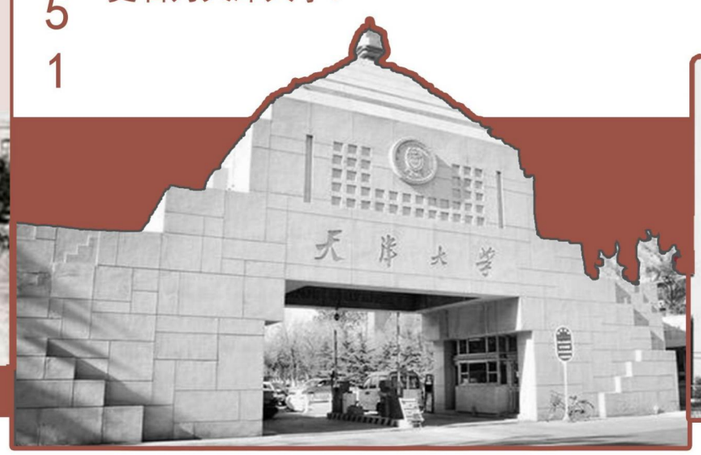

1997年6月，天津大学进行学院制改革，

在原建筑系的基础上，成立了天津大学

建筑学院。



1951



1928

成立于1928年的华北水利委员会，

在华北水利委员会主持的会议中，

提出了设立“河工试验室”的建议。



天津大学水力实验室始创于

1952年，是我国高校中创立

较早的水力实验室之一。




1952

2015年天津大学水力实验室搬迁至天津大学北洋园校区，

原场地由建筑学院继续使用。

1928

· 基地周边业态

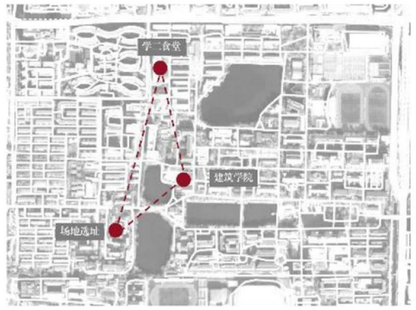






本次设计选址于天津市南开区天津大学水利馆原址，场地紧邻天津大学西门，现部分为天津大学建筑学院用地。场地紧邻天津大学西门，与湖滨路相接，人流量大且内部交通流线不畅；周边液态以教学区域、商业店铺以及居民住宅为主，液态较为丰富。

· 场地现存问题

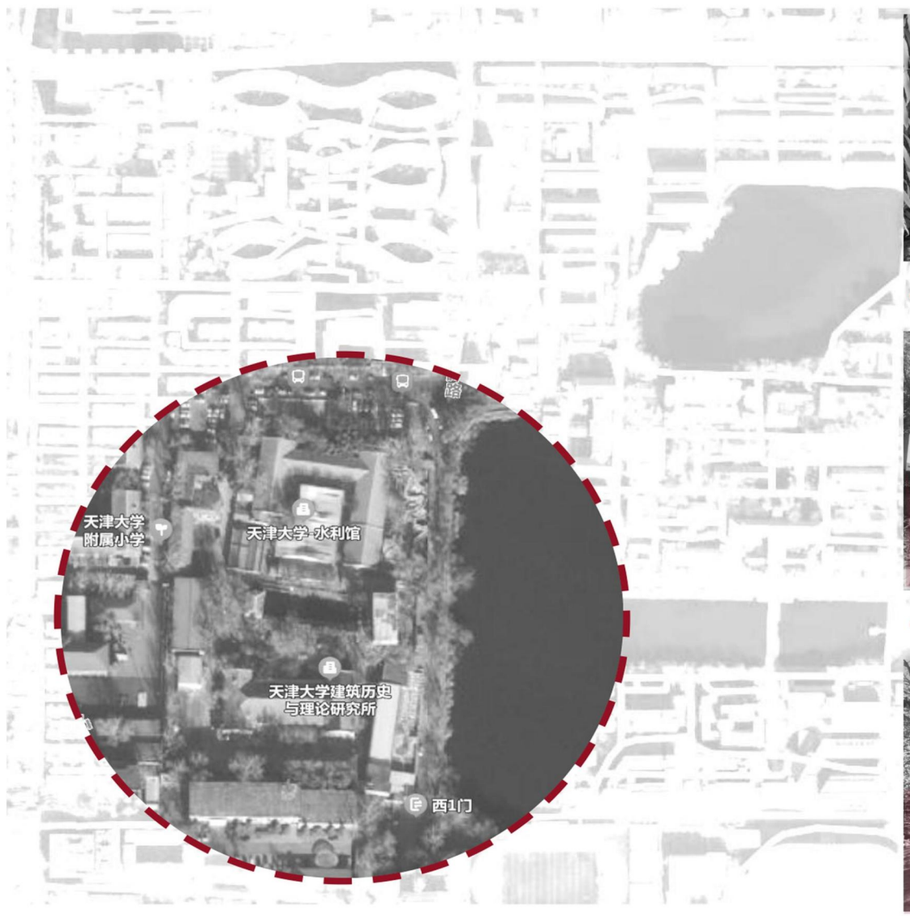

· 东侧湖景未得到良好运用，人与水缺乏互动







· 活动设施简陋，缺乏公共空间








· 步行道理不畅，人车混行








· 总平面图 1:1000

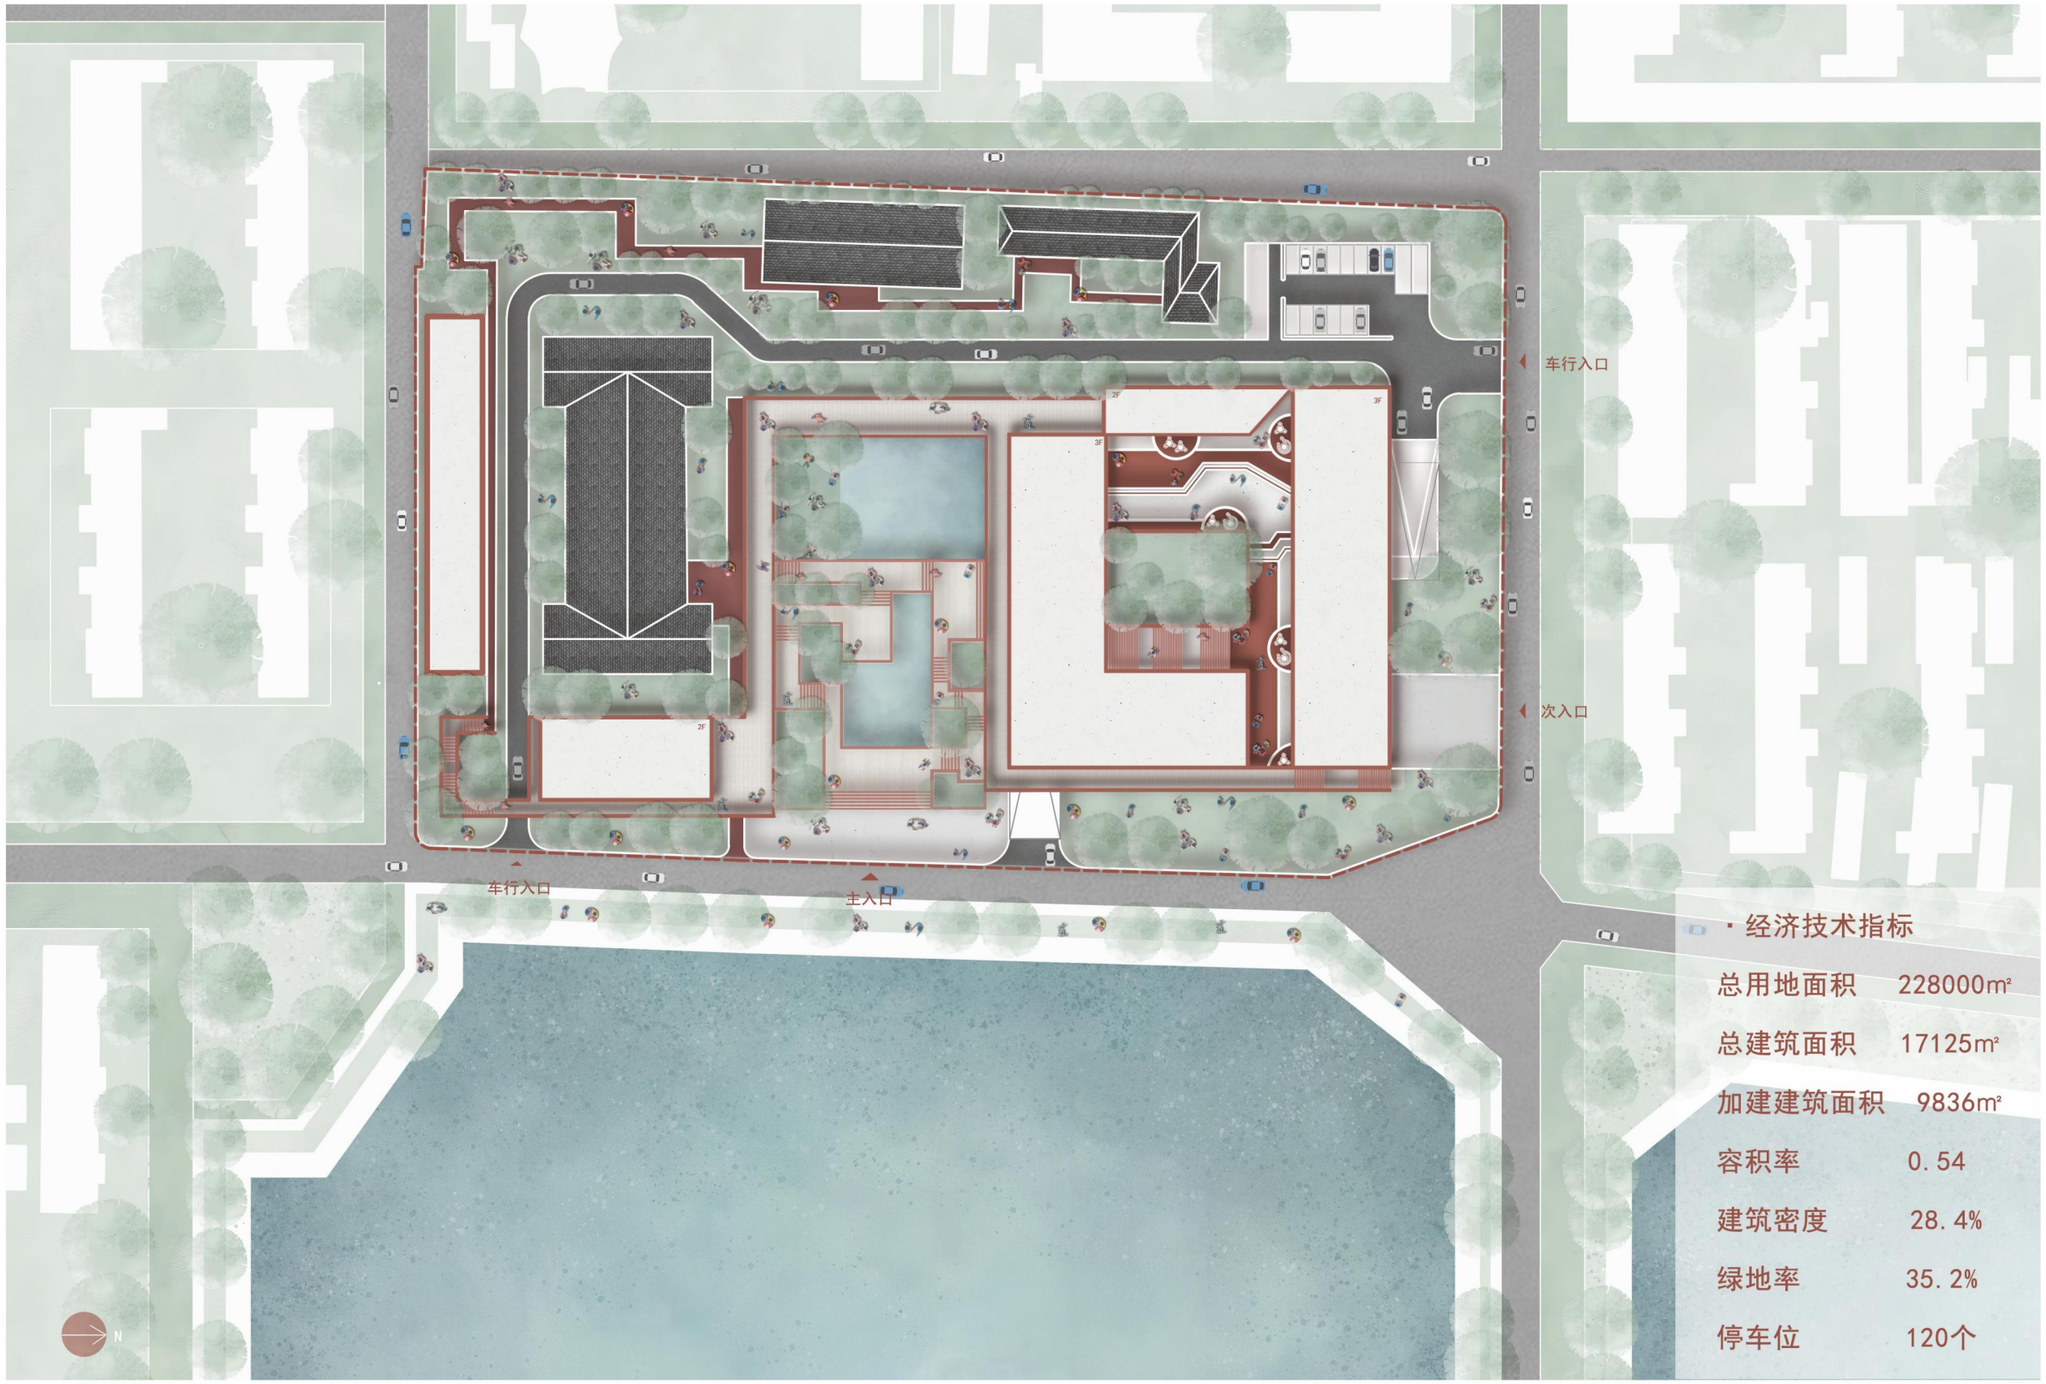

· 经济技术指标

总用地面积	228000m²
总建筑面积	17125m²
加建建筑面积	9836m²
容积率	0.54
建筑密度	28.4%
绿地率	35.2%
停车位	120个

· 爆炸分析图

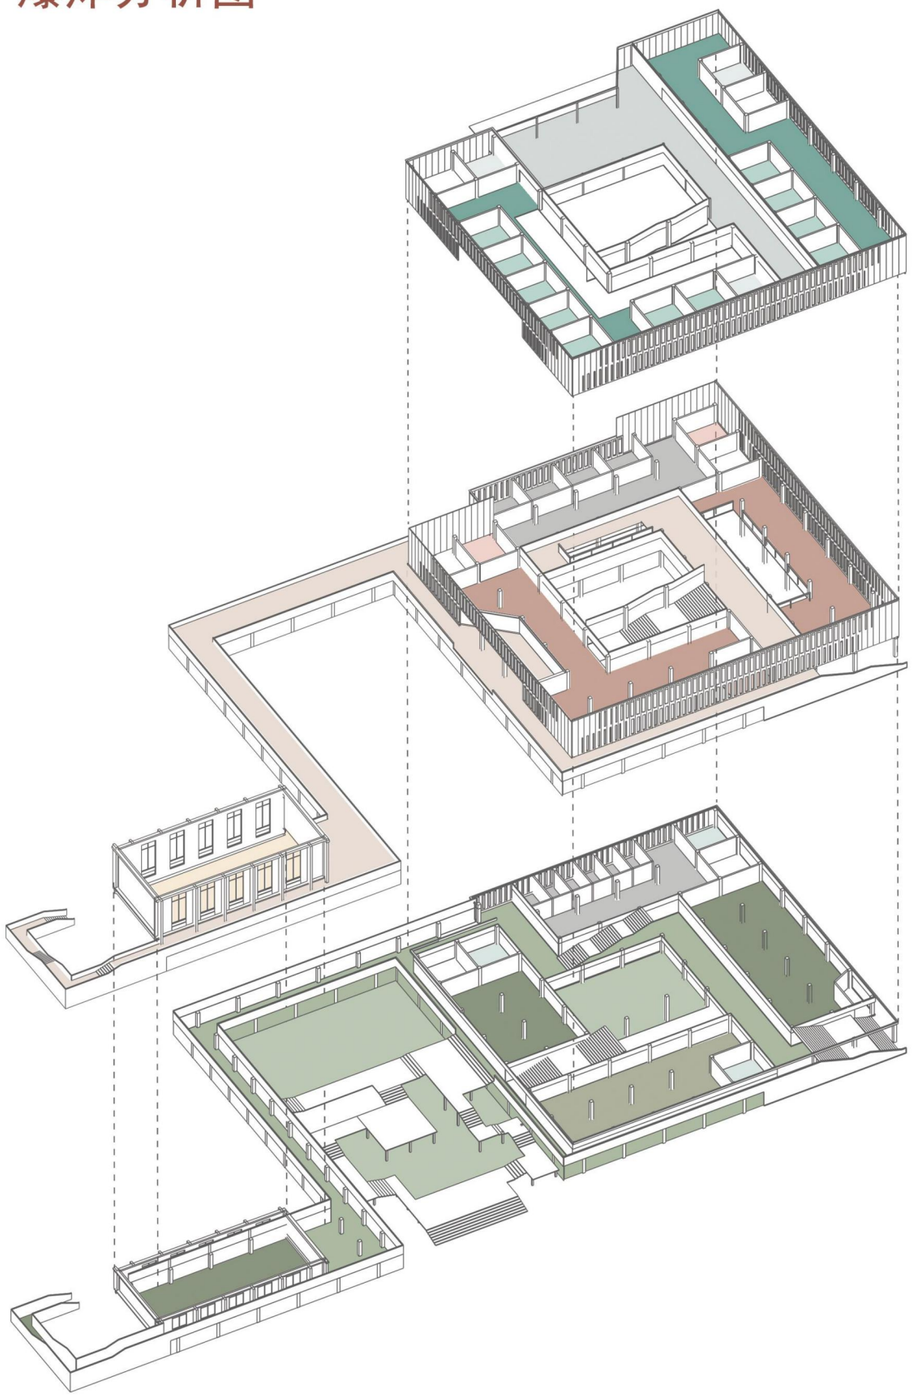


室外活动区
私密学习区
公共学习区

行政用房
讲座展览区
公共洽谈区
多功能活动区

研究用房
户外活动区
餐饮洽谈区
多功能活动区

· 空间分析

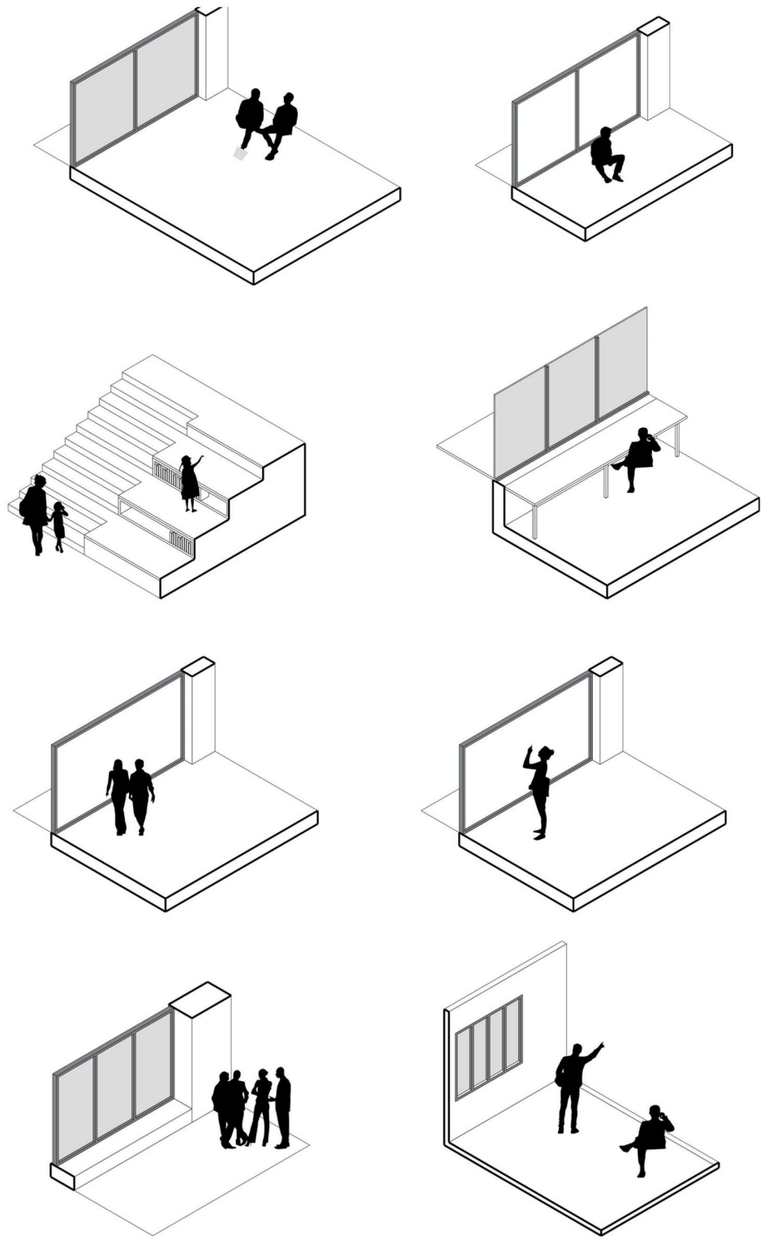


· 东立面图 1：500



· 1-2剖面图 1：500



· 整体鸟瞰图

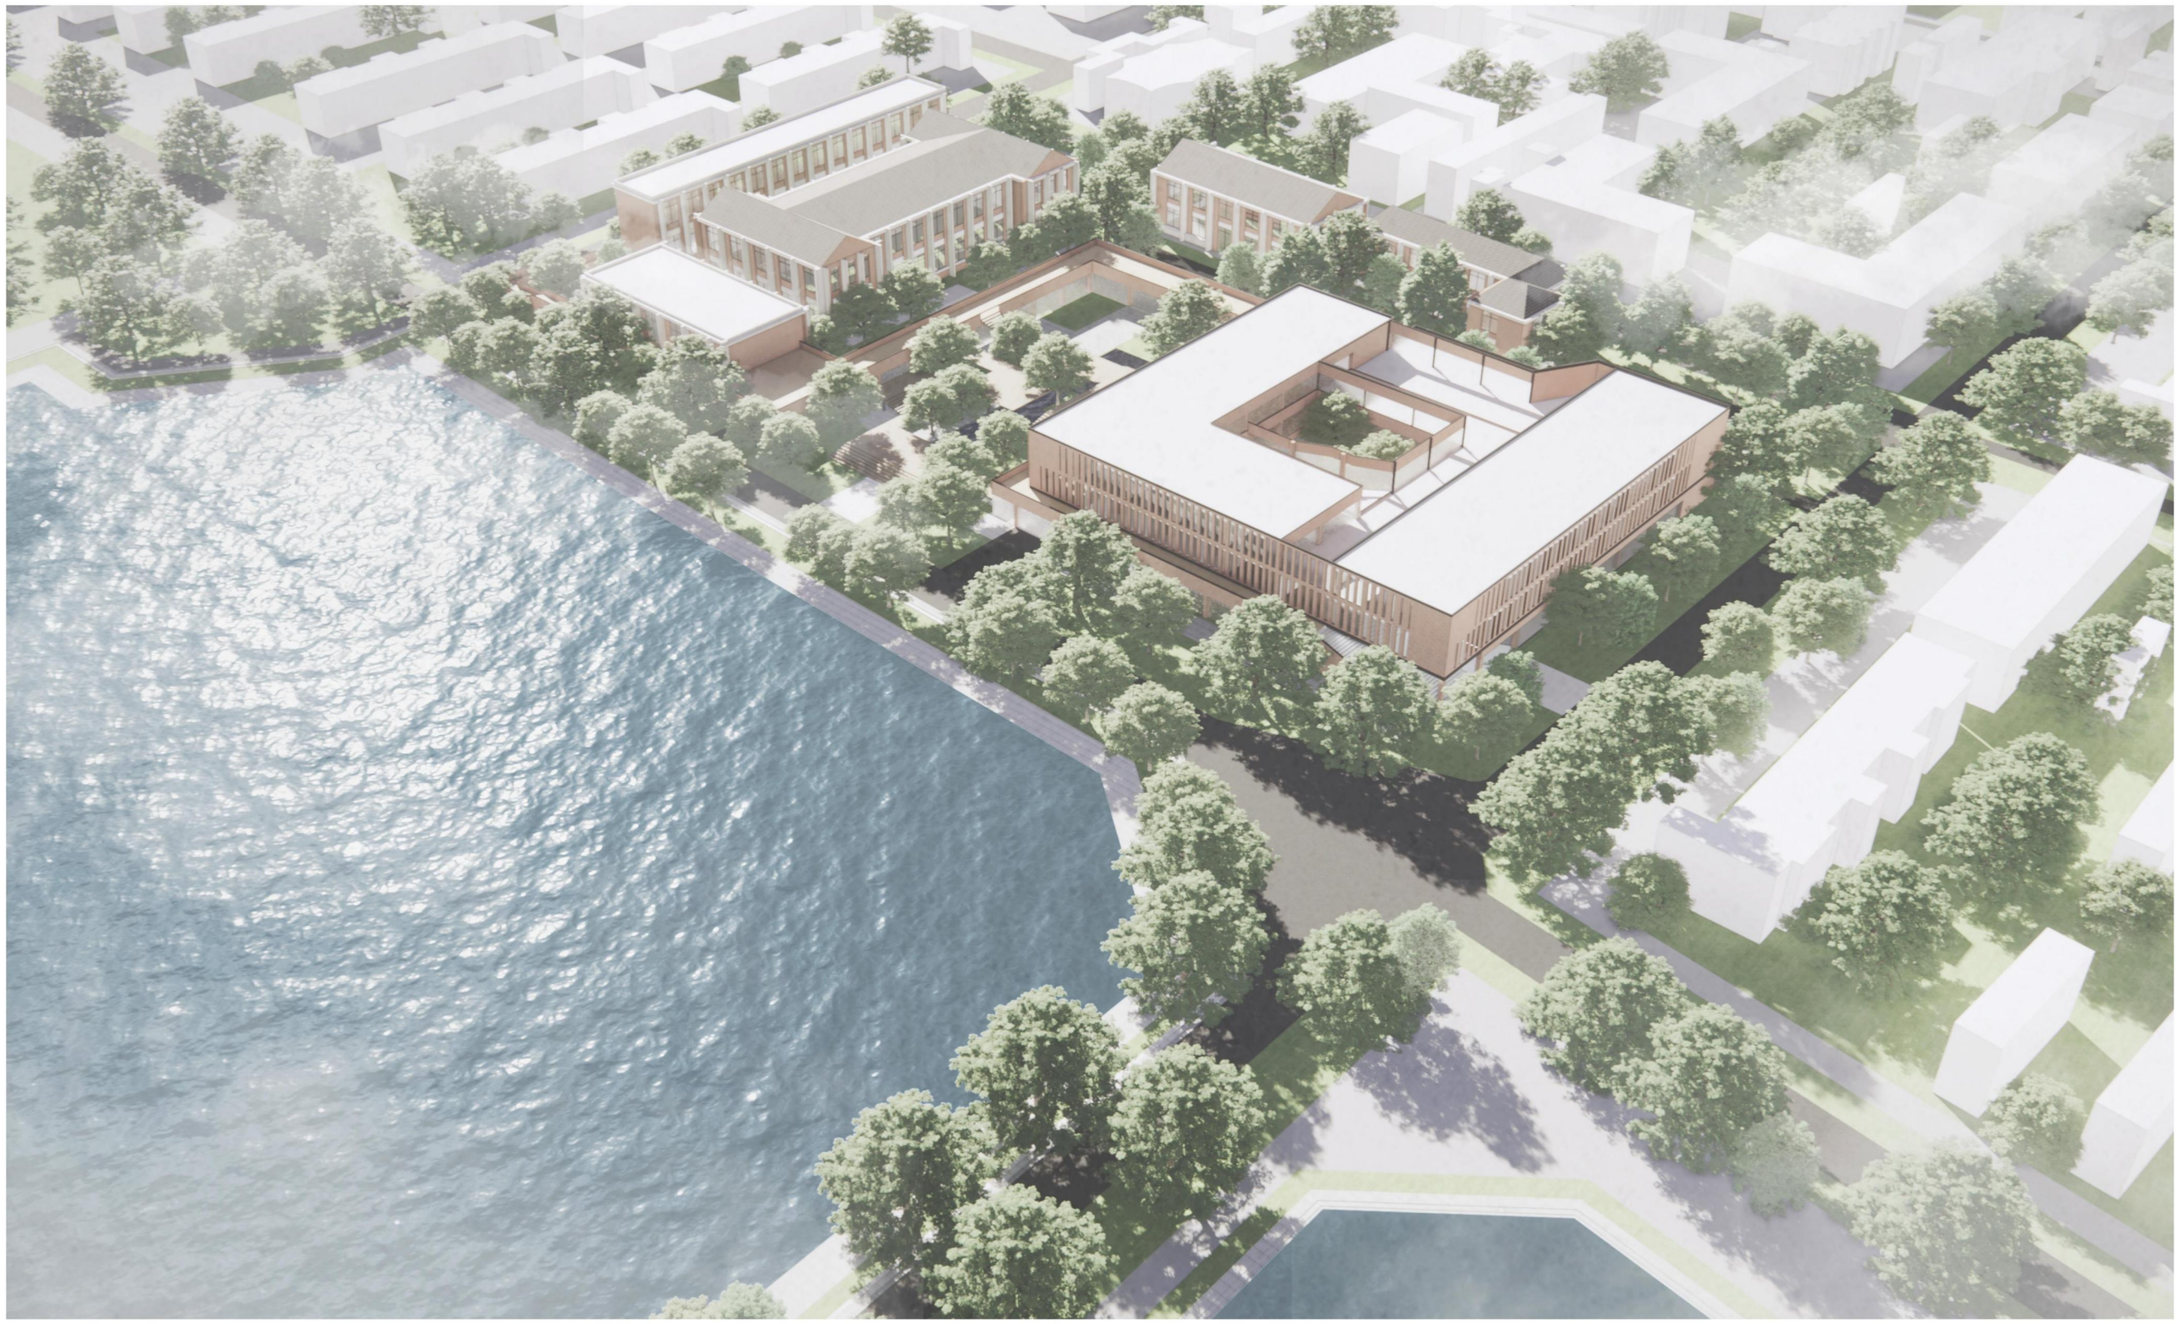

· 室外平台效果图



· 清晨效果图

